План прокладки кабеля и размещения оборудования

б/м

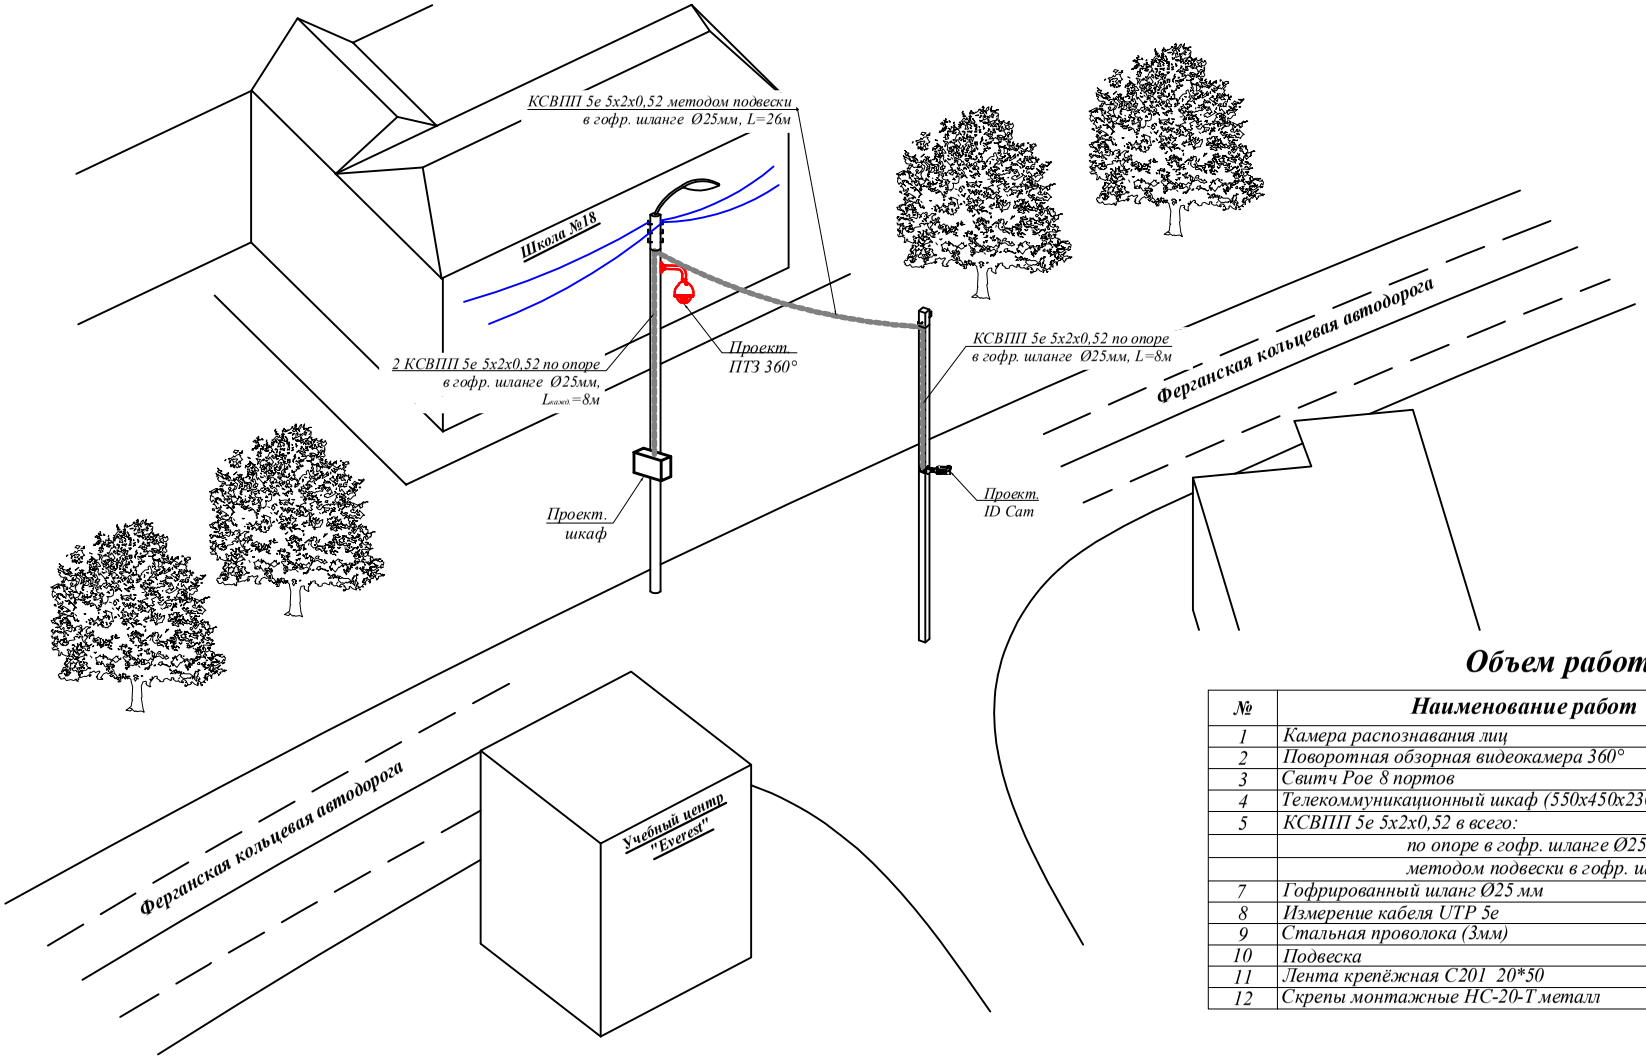

Объем работ

№	Наименование работ	Ед.изм.	Кол-во
1	Камера распознавания лиц	шт	1
2	Поворотная обзорная видеокамера 360°	шт	1
3	Свитч Poe 8 портов	шт	1
4	Телекоммуникационный шкаф (550х450х230)	шт	1
5	КСВПП 5е 5х2х0,52 в всего:	м	50
	по опоре в гофр. шланге Ø25 мм	м	24
	методом подвески в гофр. шланге Ø25 мм	м	26
7	Гофрированный шланг Ø25 мм	м	50
8	Измерение кабеля UTP 5е	шт	2
9	Стальная проволока (3мм)	Тн	0,00143
10	Подвеска	шт	26
11	Лента крепёжная С201 20*50	м	4
12	Скрепы монтажные НС-20-Т металл	шт	4

б/м

УСЛОВНЫЕ ОБОЗНАЧЕНИЯ:

- PTZ камера;
- ID камера;
- проектируемое оборудование;
- лицевая сторона оборудования;
- проектируемый UTP 5е кабель;

Изм.	Кол.уч.	Лист	№ док	Подпись	Дата	00041 - 1 - ВН -03			
						«Внедрение интеллектуальной системы видеонаблюдения в МСГ, районах Наманган, Уйчи и Косонсой Наманганской области»			
					2024	IP-Видеонаблюдение (объект: район Уйчи, МСГ Мавжуд, городок Жийдакапа)	Стадия	Лист	Листов
							РП	1	
Нач.отдела		Саламов Ж.				План прокладки кабеля и размещения оборудования	SCC г.Ташкент		
Исполь.		Базарбаева							
Н.контр.		Тураев Ж.							